

SHEET LIST			
Sheet Number	Sheet Name	Revision	Revision Date
A01	COVER SHEET	A	16/05/2024
A02	SITE PLAN	A	16/05/2024
A03	STREET ELEVATIONS	A	16/05/2024
A04	RECEPTION AREA	A	16/05/2024
A05	SOLAR STUDY	A	16/05/2024



ASSESSMENT NAME
OFFICE BUILDING

ASSESSMENT NUMBER
AT3


STUDENT NUMBER
20068456

STUDENT NAME
JAANA BLINOVA

LECTURER
JESUS ZIEGLER



BUILDING DESIGN AND
TECHNOLOGIES
Level 3, 30 Aberdeen Street,
NORTHBRIDGE 6003, WA
Tel. (08) 9242 0455

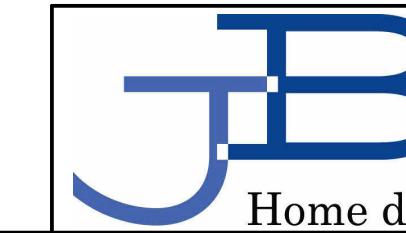


BUILDING DESIGN AND TECHNOLOGIES
Level 3, 30 Aberdeen Street,
NORTHBRIDGE 6003, WA
Tel. (08) 9242 0455

WORKING DRAWINGS
Assessment Name:
OFFICE BUILDING

Drawing Title: **SITE PLAN**
Project Details: Julie Williams
Lot 1 Corner of Great Eastern Hwy and Leake Street

Name:	JAANA BLINOVA	Assessment	AT3
Student ID:	20068456	Rev.	
Scale:	As indicated	Dwg Rev.	
Lecturer:	JESUS ZIEGLER	Date:	A02 A
REV	Description	Date	22/05/2024 10:07:29 PM

Assessment.
(circle)
REQUIREMENTS MET
REQUIREMENTS NOT MET

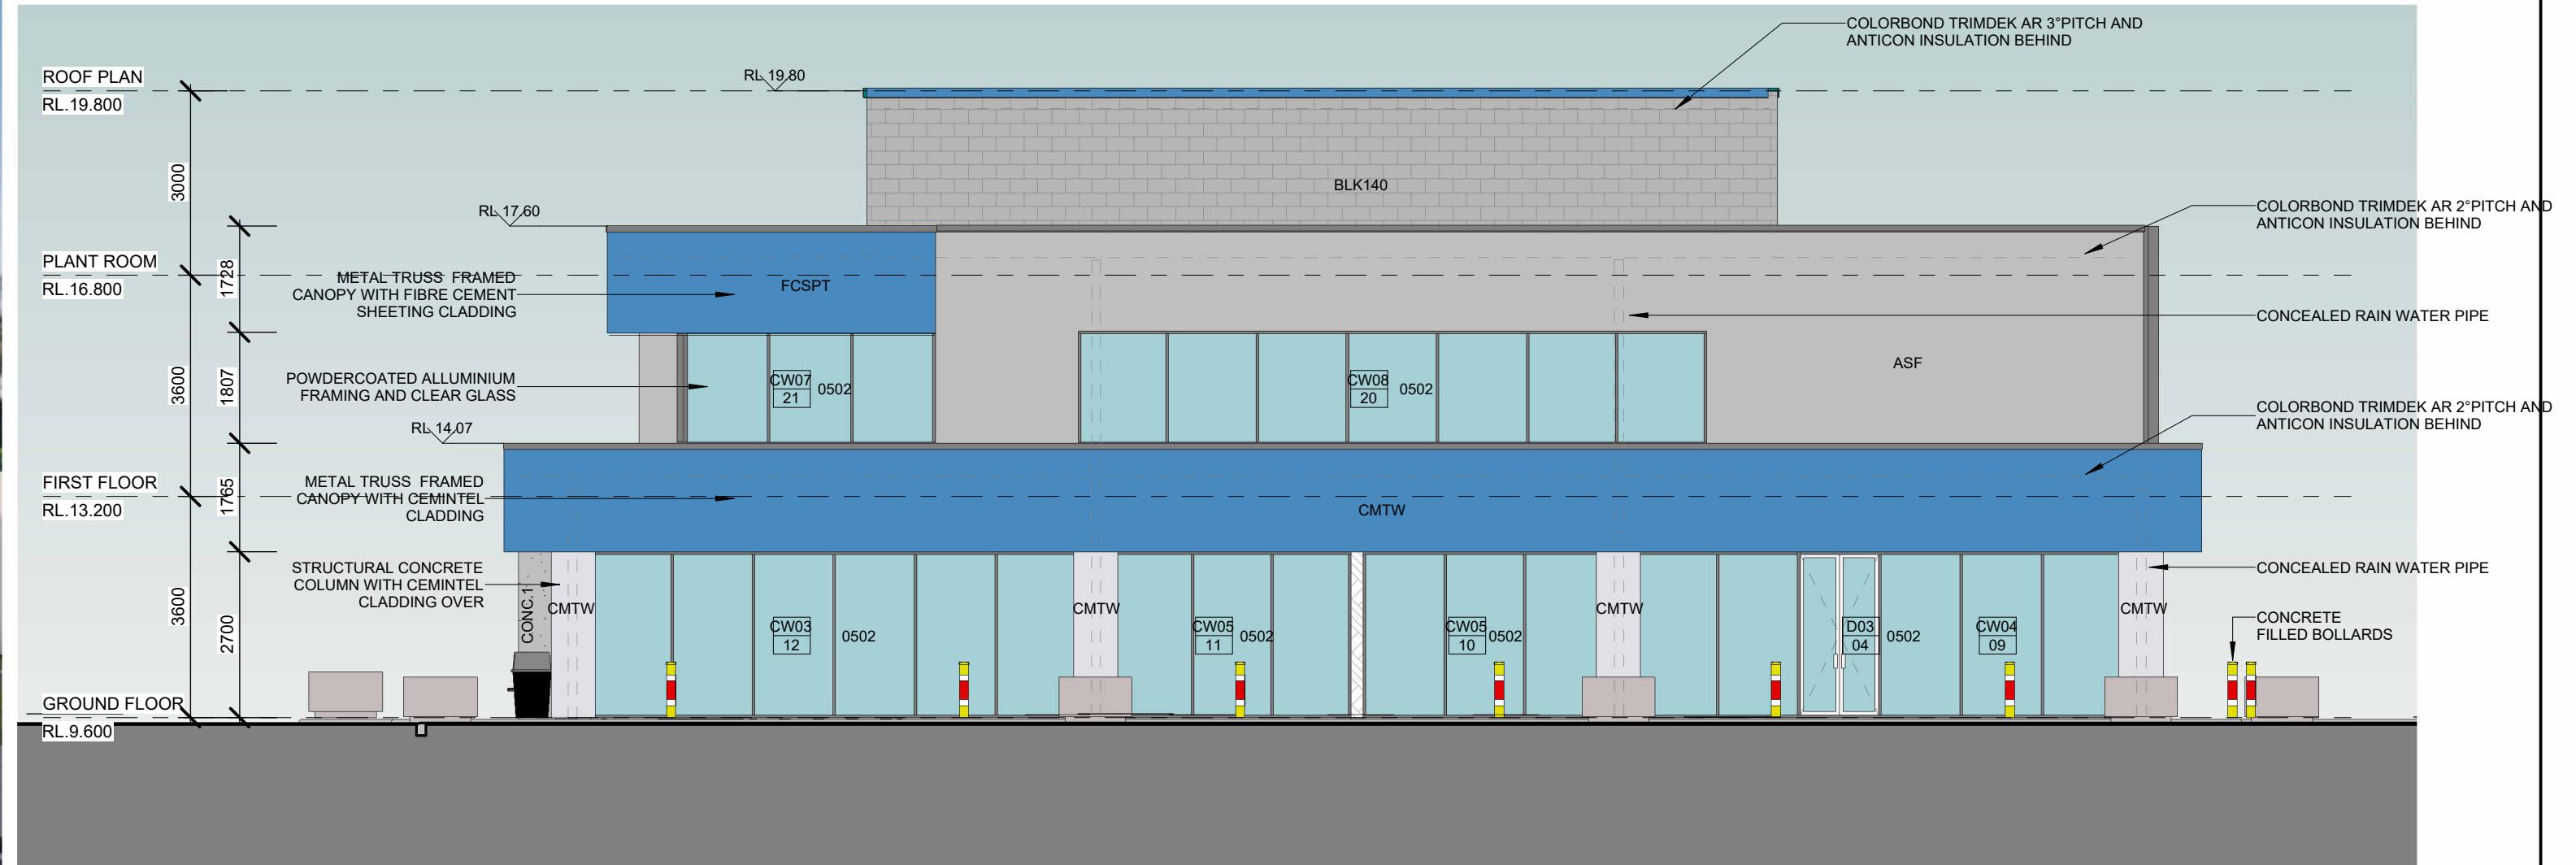

1 GREAT EASTER HIGHWAY ELEVATION
A003 SCALE: 1 : 100




2 LEAKE STREET ELEVATION
A003 SCALE: 1 : 100

WALL PAINTS SCHEDULE



COLOR SAMPLE	COLOR	MANUFACTURER
[Grey square]	WOODLAND GREY	COLORBOND
[Yellow square]	PAPERBARK	COLORBOND
[Blue square]	DOVER WHITE	COLORBOND

Key Value	Keynote Text
0502	POWDWERCOATED ALUMINIUM GLAZING SYSTEM REFER SPECIFICATION
ASF	ASF WALLING SYSTEM FLUSH AND TEXTURED PAINT FINISH AS SPECIFIED
BLK140	140 CONCRETE BLOCKWORK. PAINT FINISHED TO ALL VISIBLE FACES
CMTW	CEMINTEL CLADDING AS SPECIFIED, ON 35mm FURRING CHANNELS FIXED TO TRUSS TO STRUCTURAL ENGINEERS DRAWINGS.
CONC.1	175mm CAST INSITU CONCRETE SHEAR WALL
FCSPT	FLAT FIBRE CEMENT SHEET EXOTEC PAINT FINISH
TRH	TOILET PAPER ROLL HOLDER AS SPECIFIED

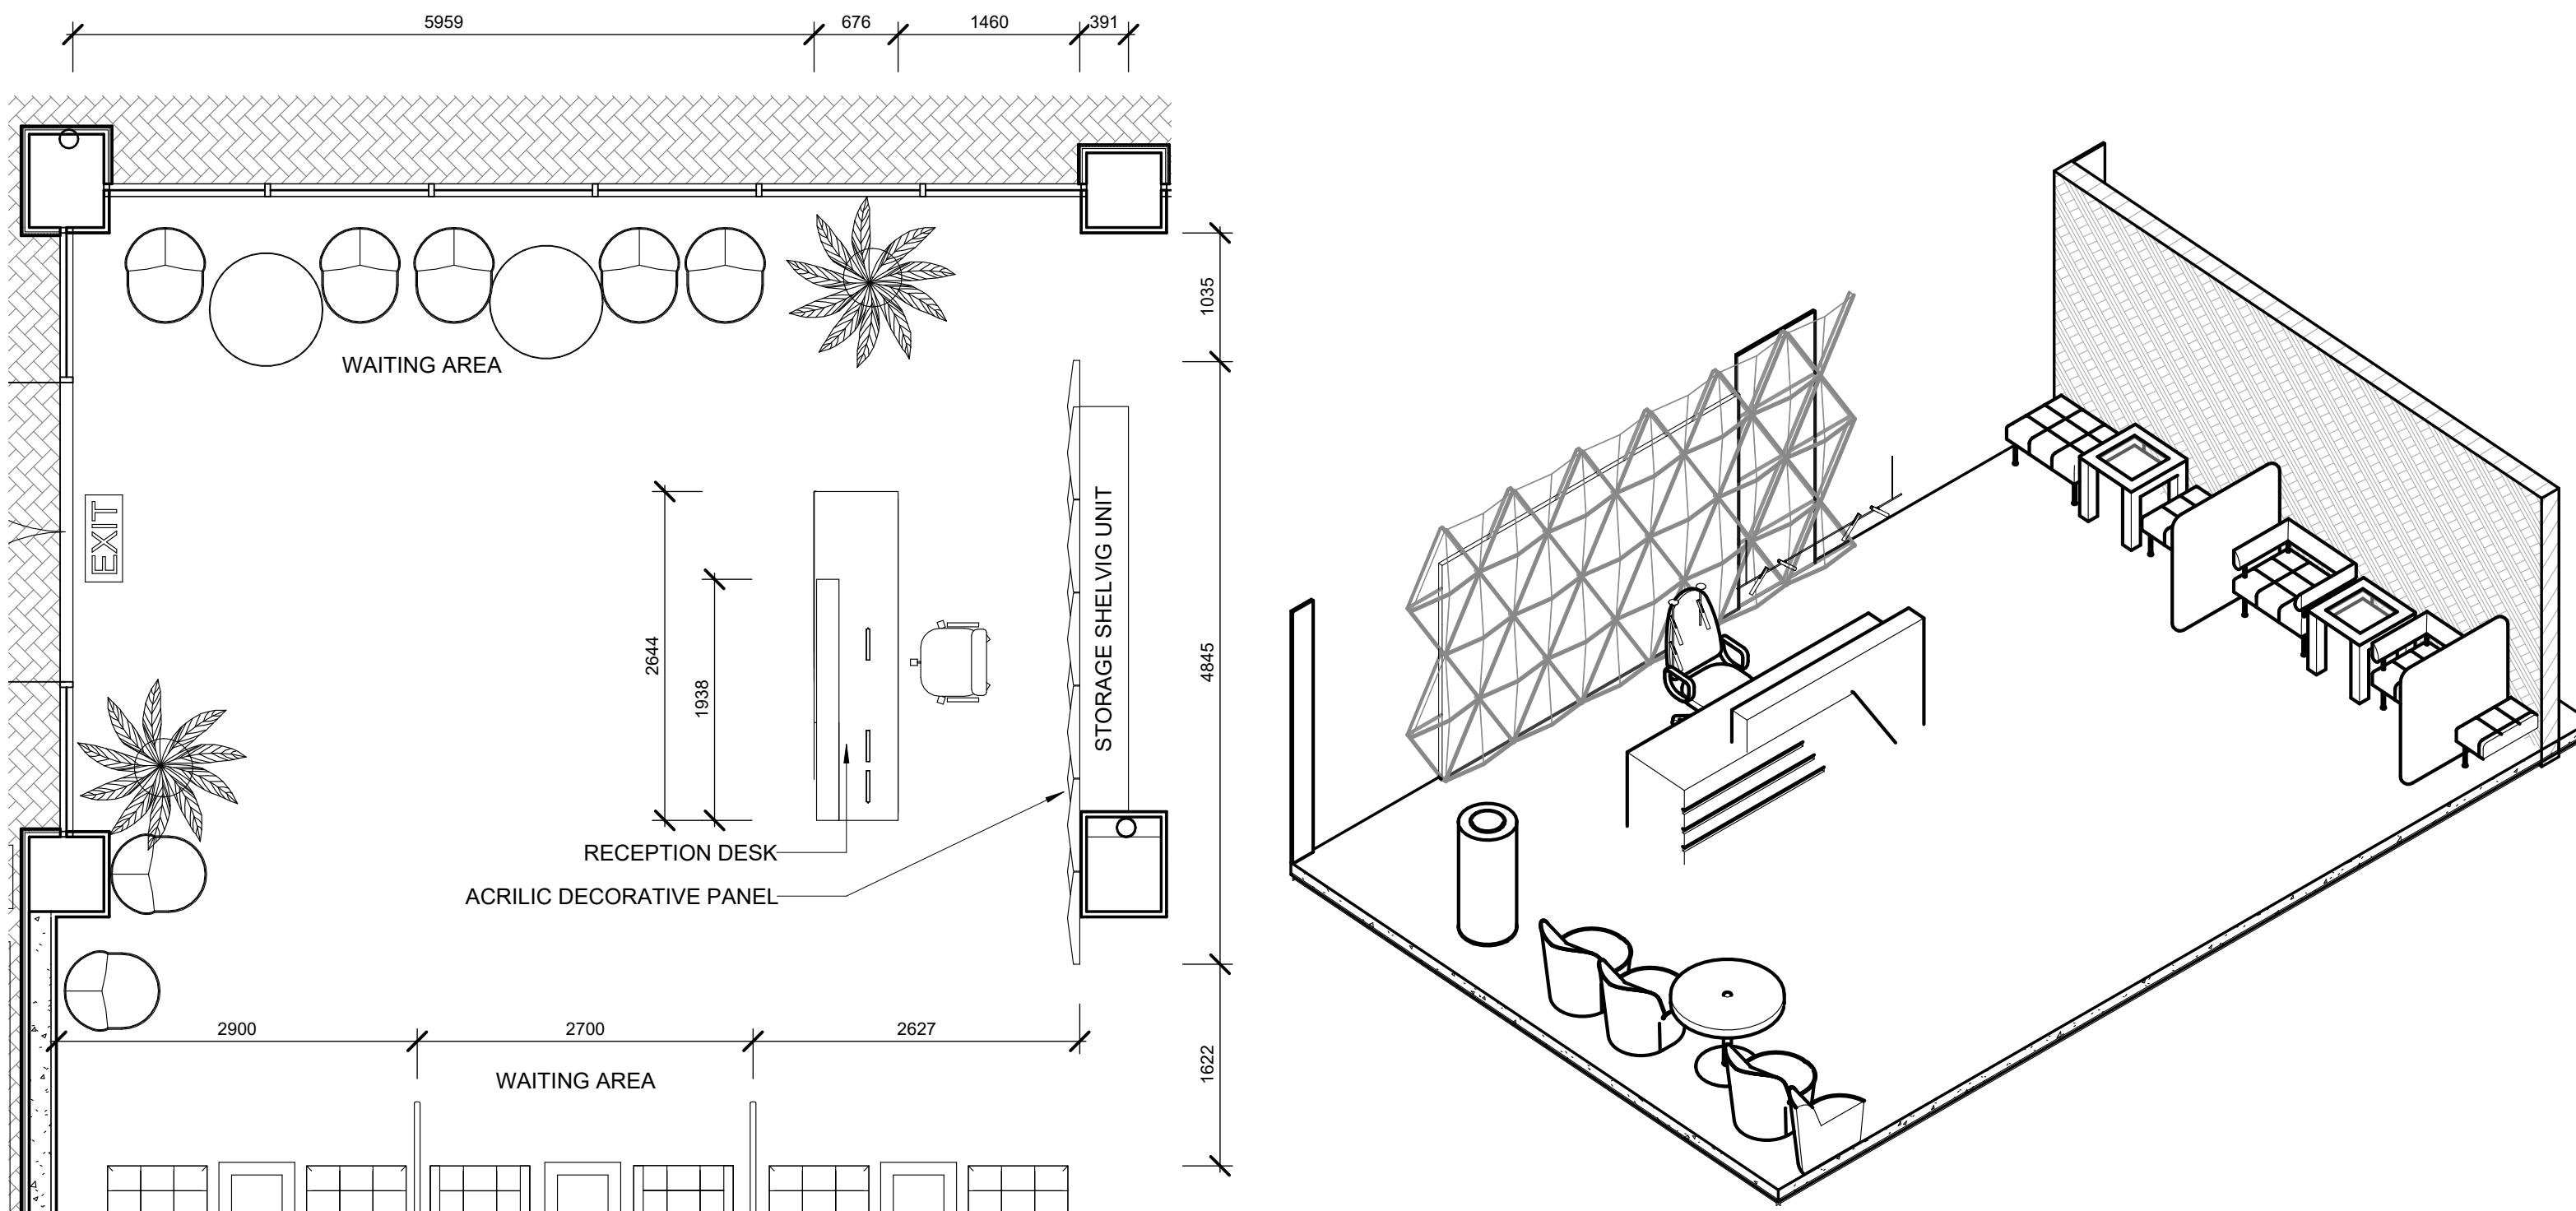


6 RECEPTION PLAN VIEW
A003 SCALE: 1:50


1 RECEPTION
SCALE:

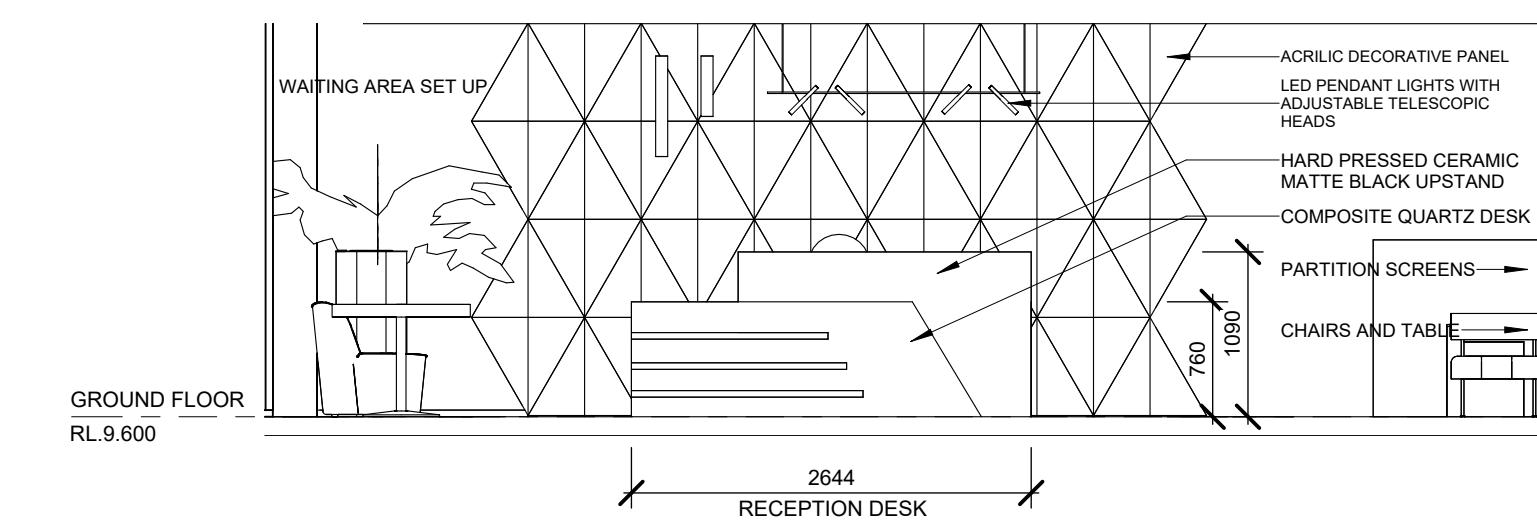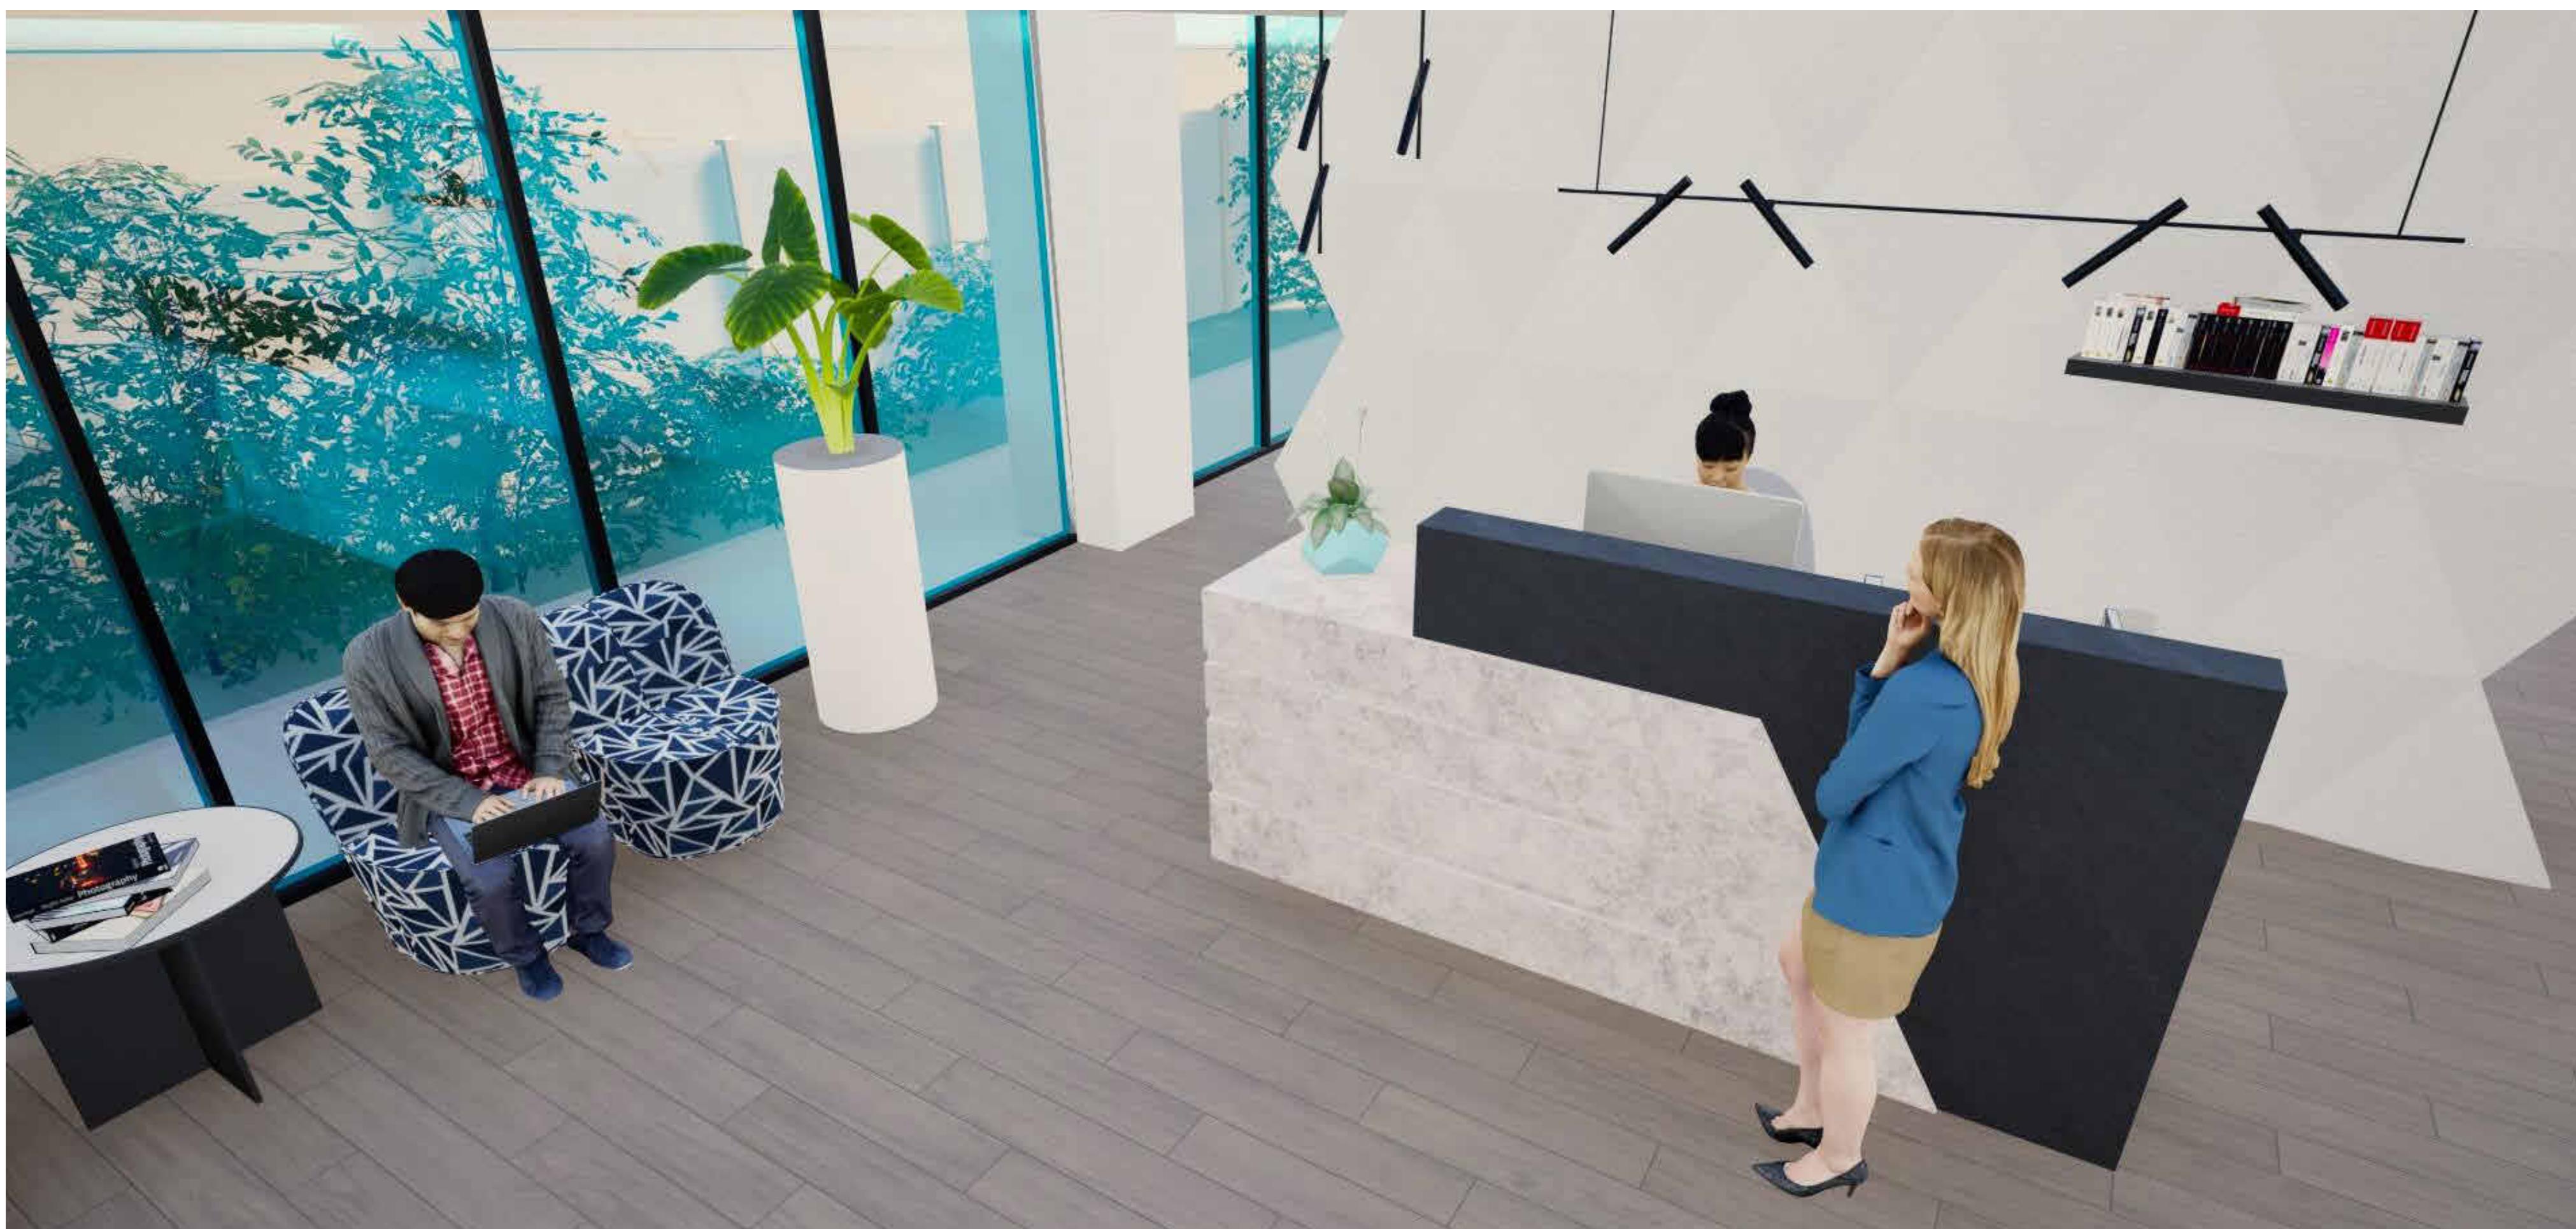



3 RECEPTION ELEVATION 1
A003 SCALE: 1:50

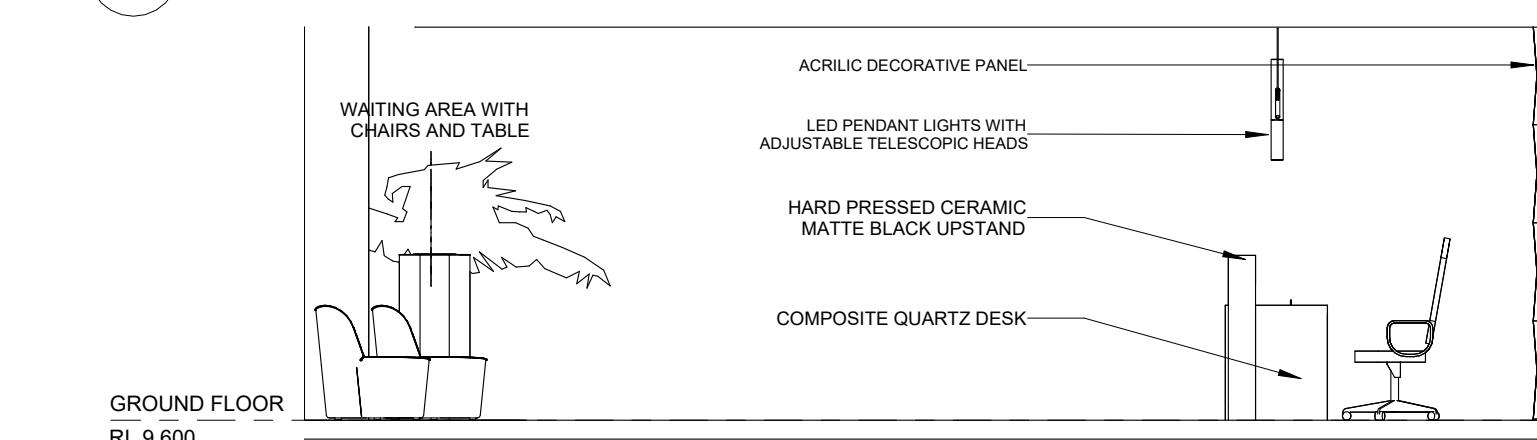


2 RECEPTION ELEVATION 2
A003 SCALE: 1:50

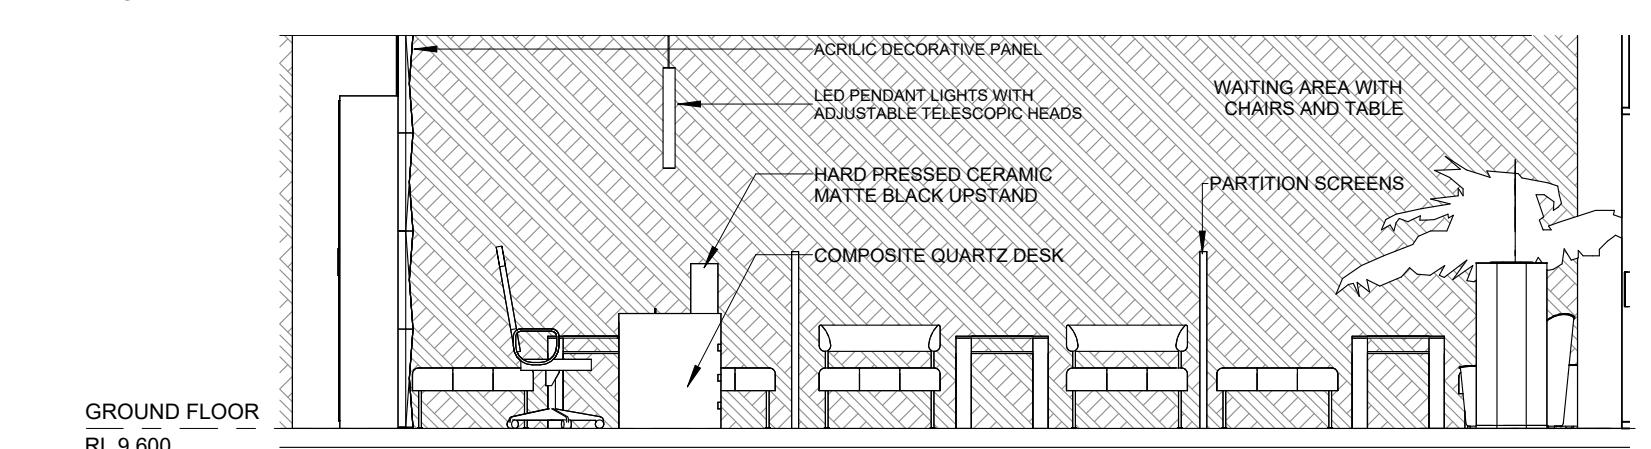

4 RECEPTION ELEVATION 3
A003 SCALE: 1:50

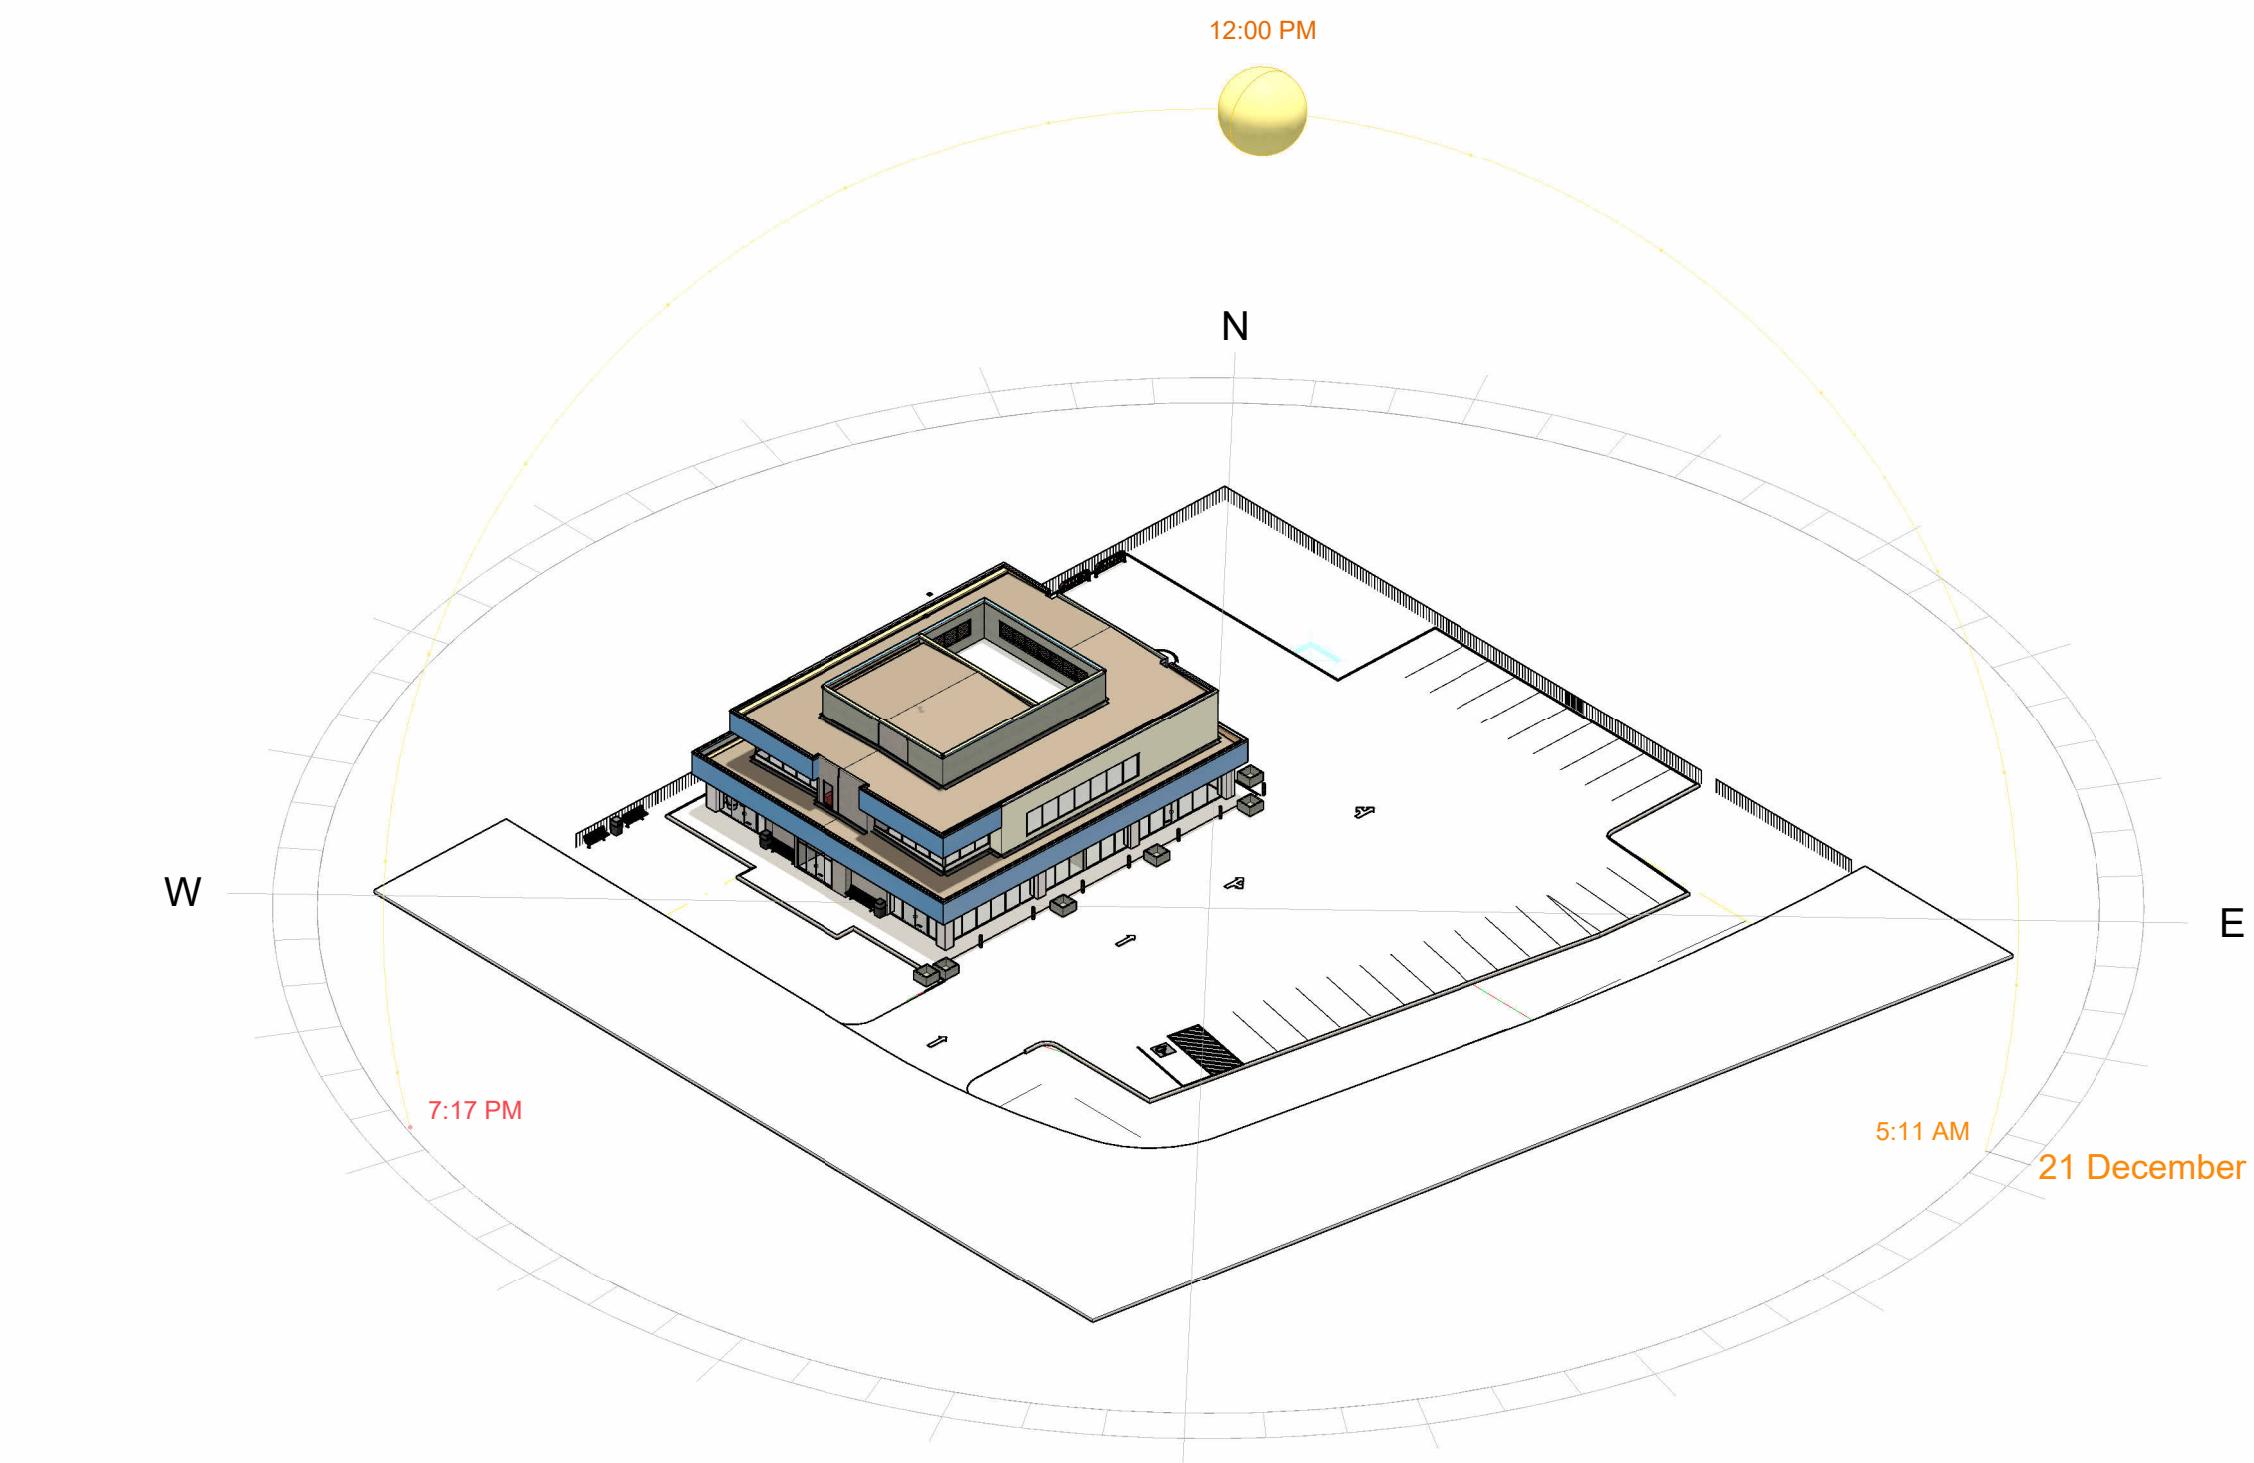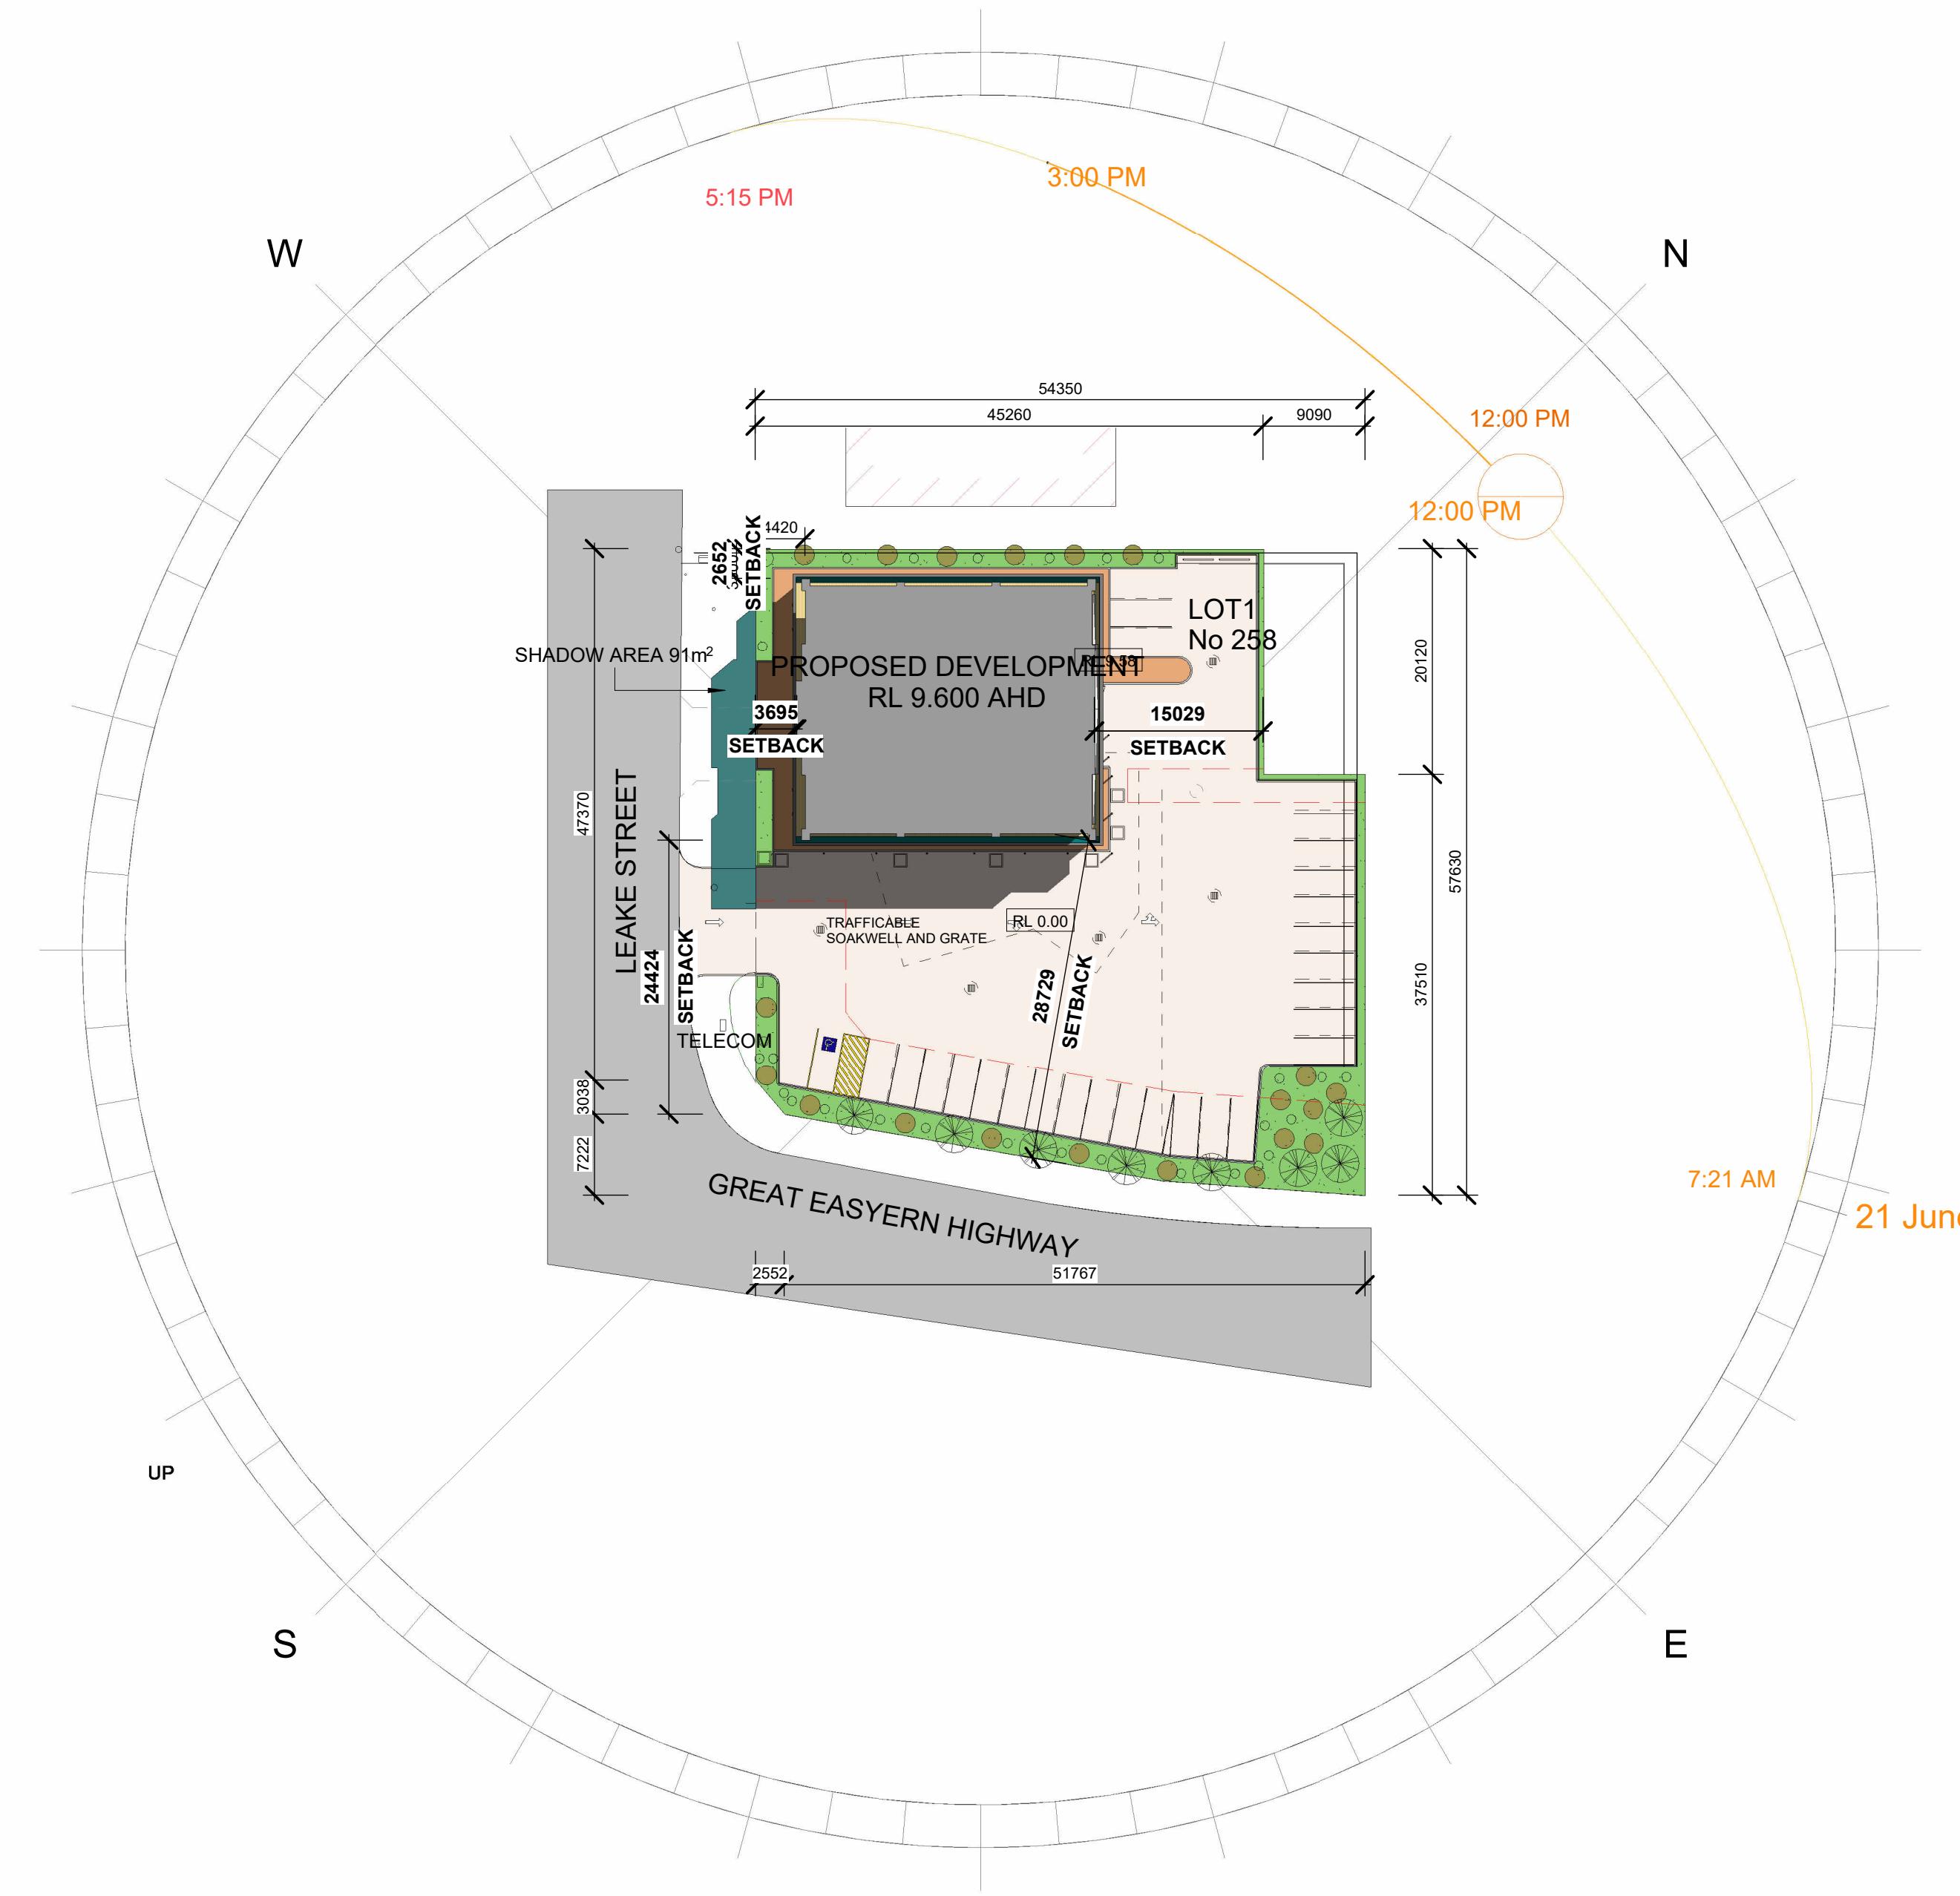

3D-SUMMER SOLSTICE-21st December 12pm

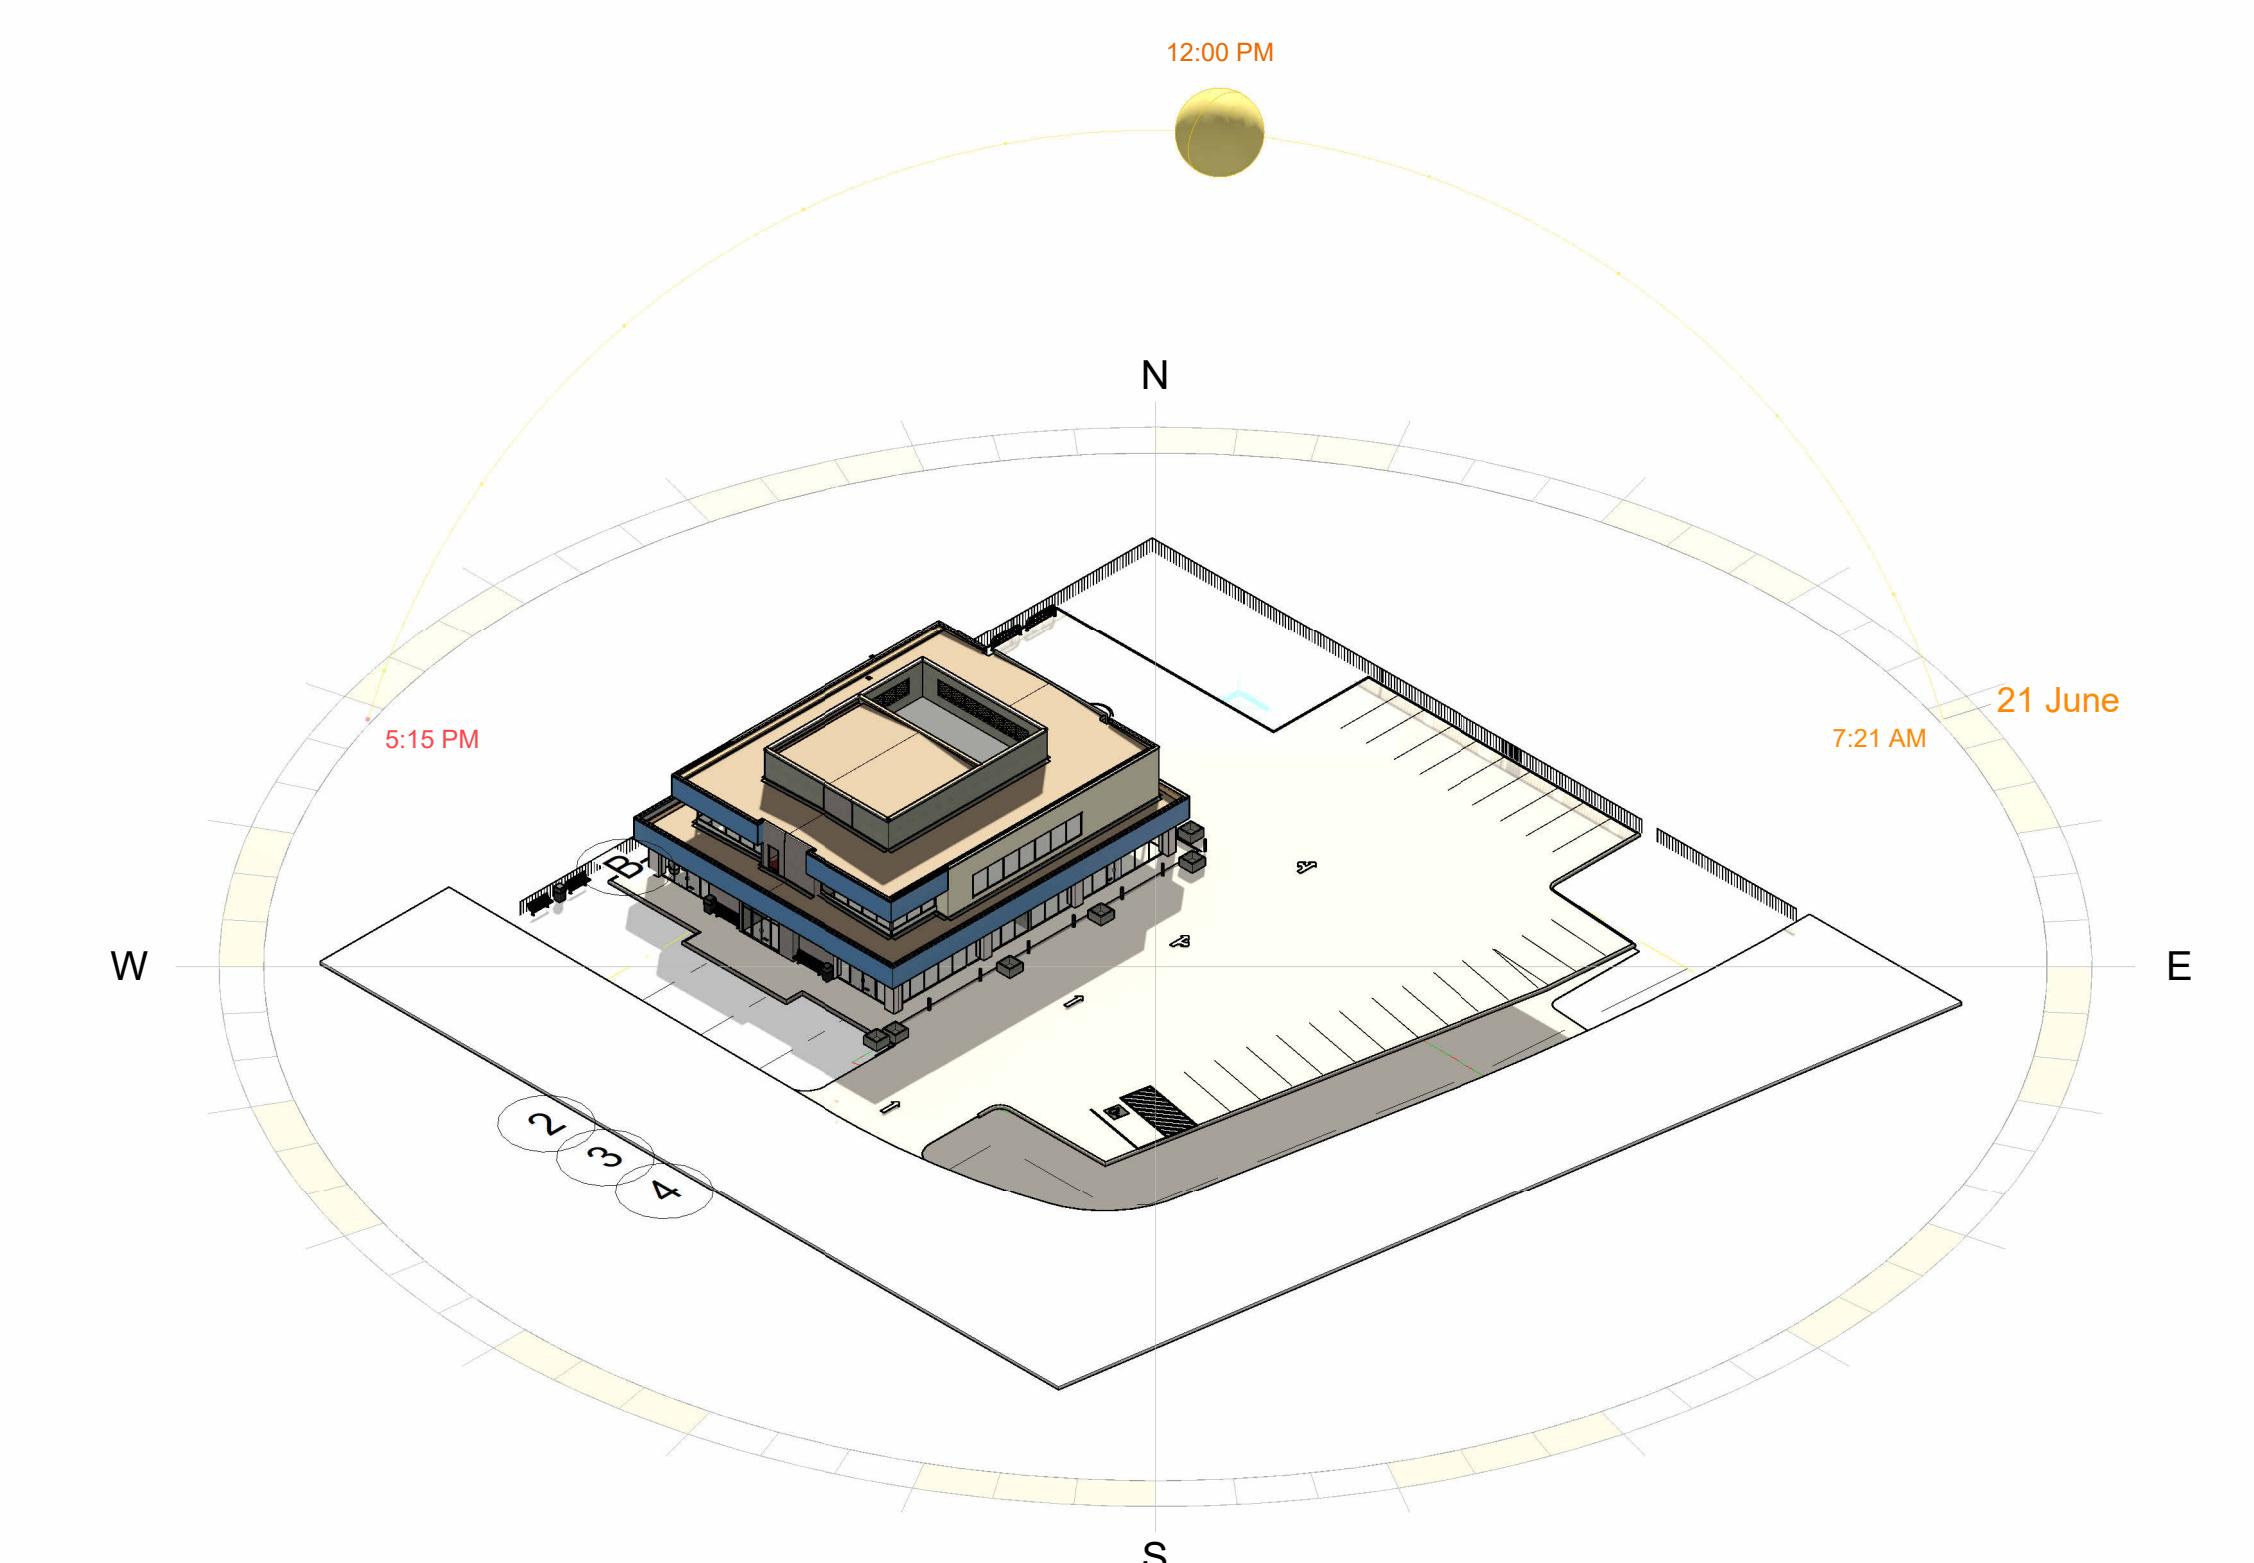

3D-WINTER SOLSTICE-21st June 12pm